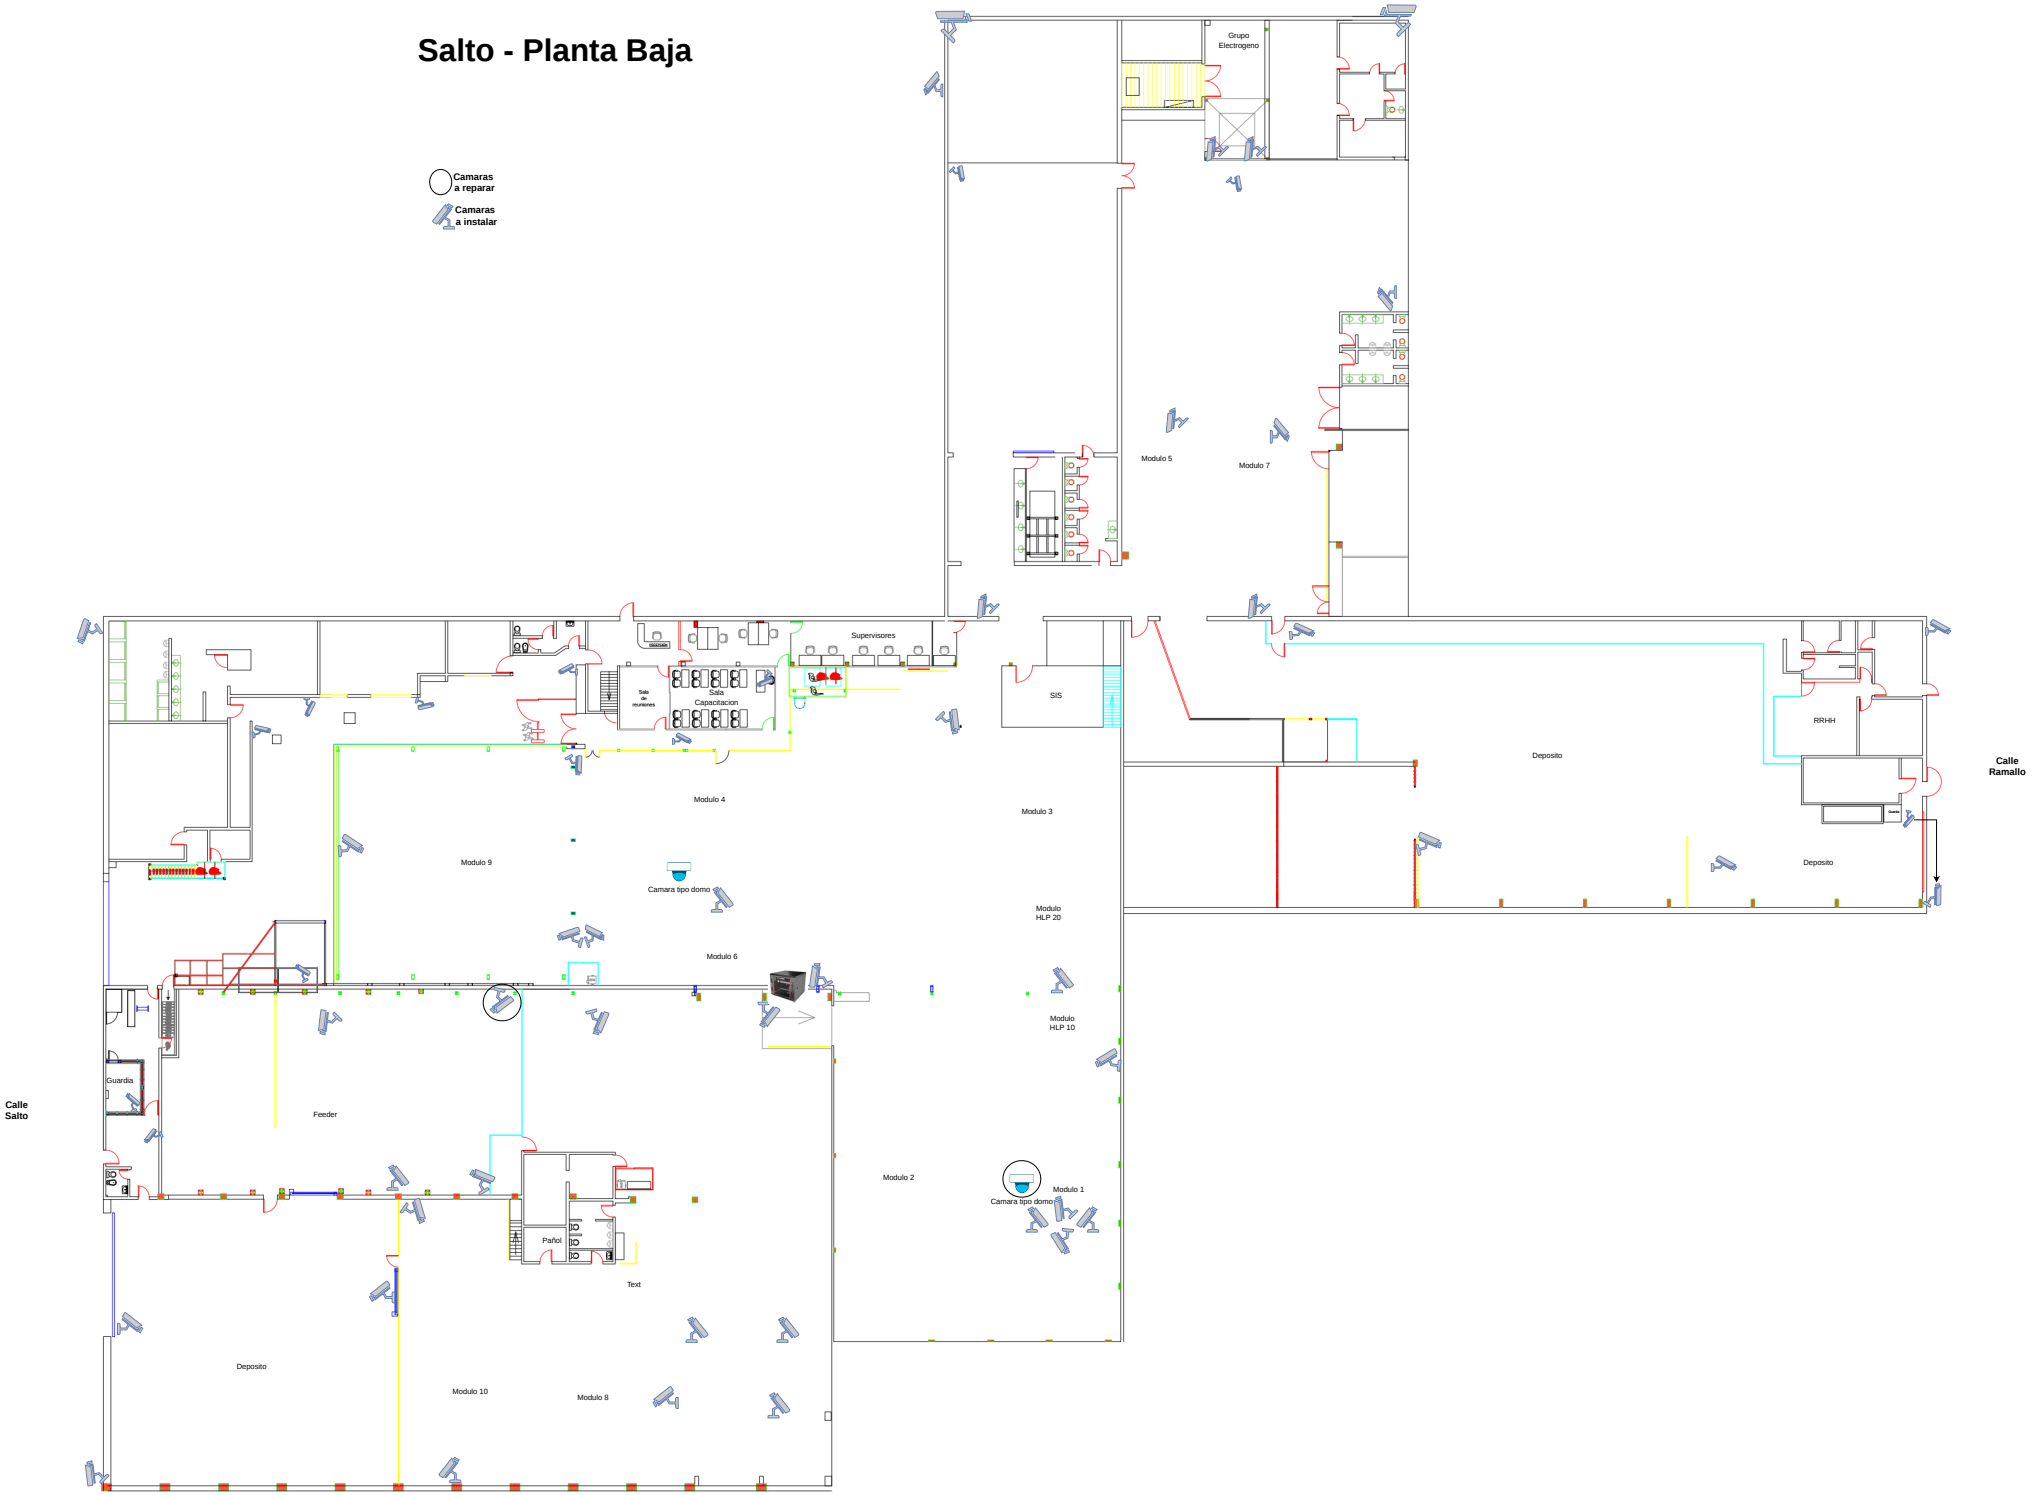Salto - Planta Baja